

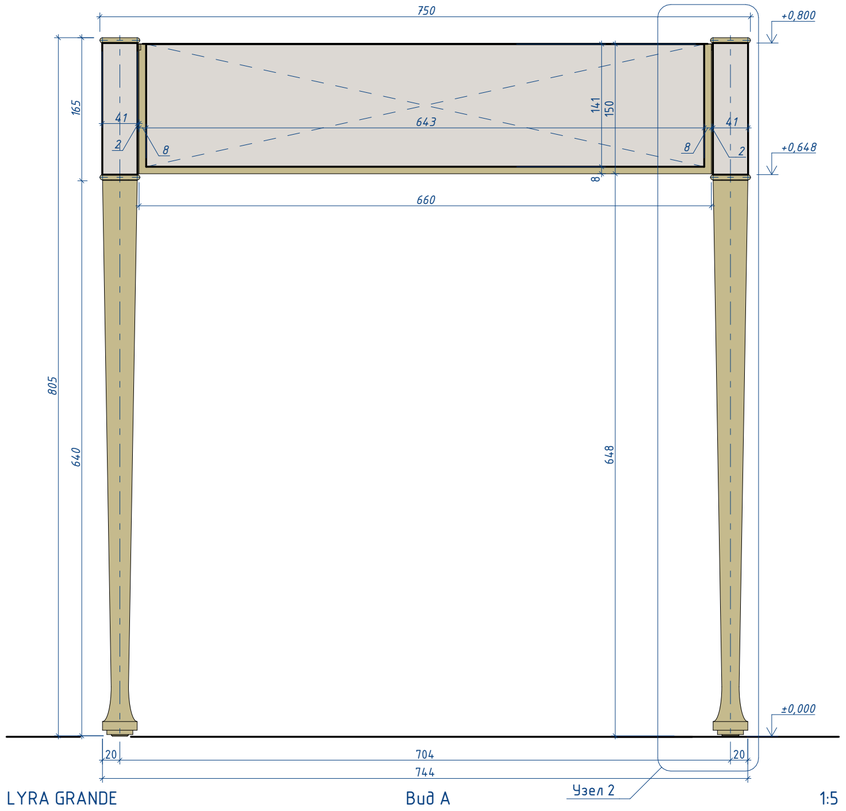


LYRA GRANDE Вид А 1:5

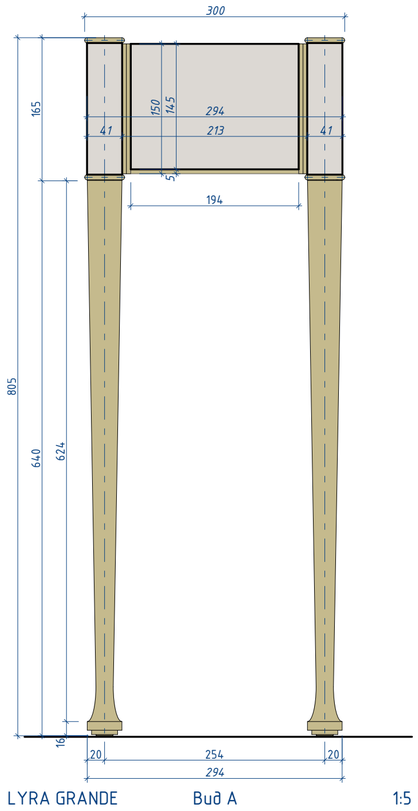


LYRA GRANDE Вид А 1:5

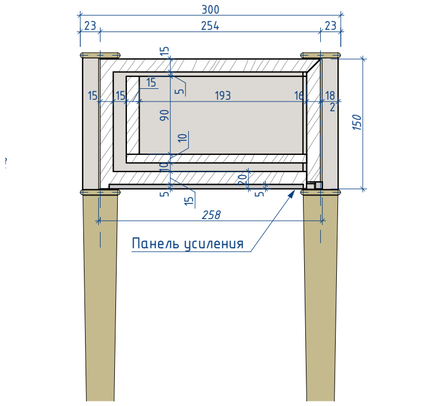


LYRA GRANDE Разрез 1 – 1 1:5




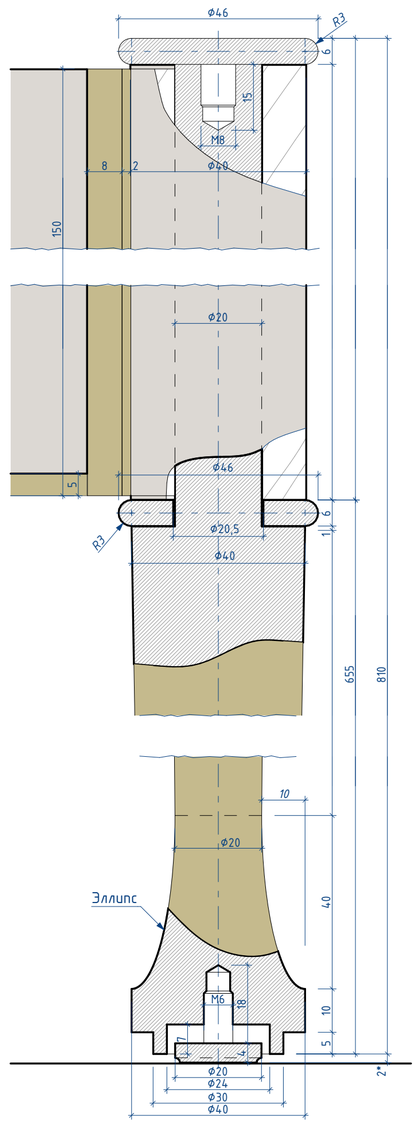

LYRA GRANDE Узел 2 1:1

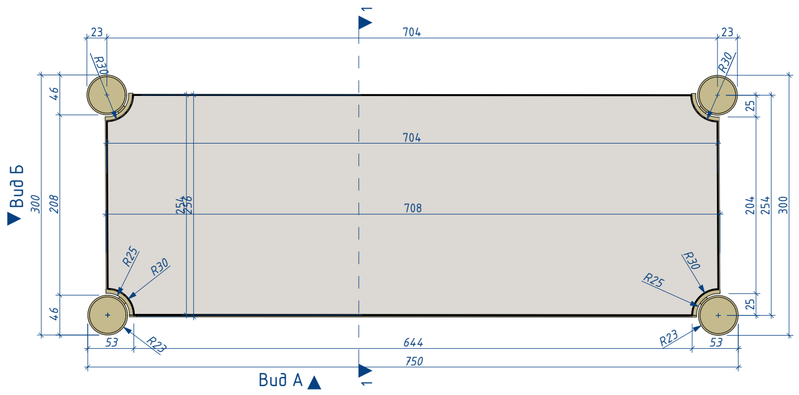

LYRA GRANDE Вид сверху 1:5

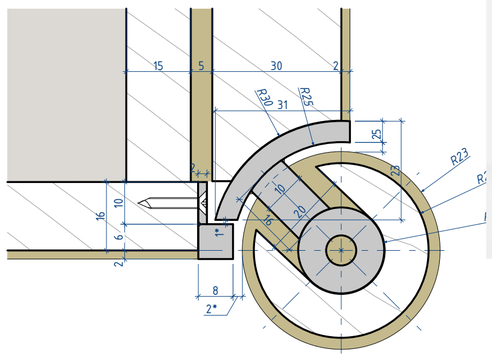


LYRA GRANDE Узел 1 1:1

ФИНИШИ LYRA GRANDE	
Цвет	Название
	– Бронза тёмная
	– Шпон клён птичий глаз

МАТЕРИАЛЫ

Штриховка	Название материала
	МДФ
	Металл

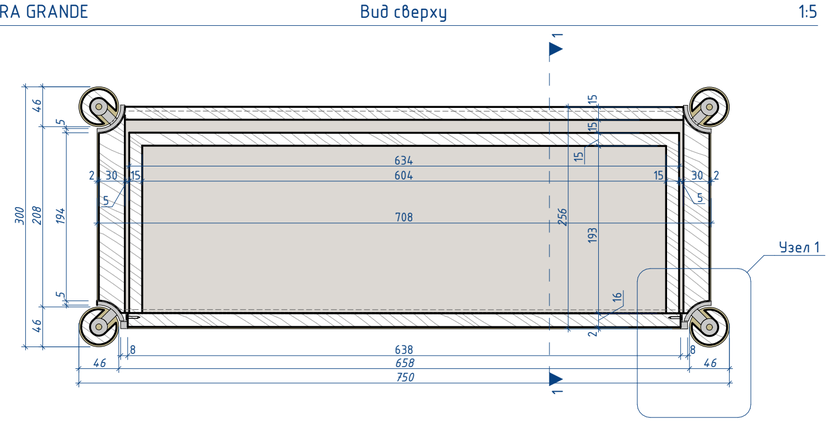

LYRA GRANDE План на отм. +0.700 1:5

1. Высотные отметки изделия даны от уровня чистого пола.
2. Индивидуальное изделие выполняется по чертежам фирмы изготовителя.
3. Все расхождения в размерах на этапе изготовления ИИ согласовать с архитектором.
4. Лаковые поверхности выполнить с закрытыми порами (при наличии таковых).
5. Финишное покрытие не должно создавать больших радиусов и наплывов на внешних и внутренних гранях и углах изделия. Грани изделия должны быть четкие, выполнены с минимальной технолгической фаской при необходимости.

		Подп.	Дата		Стадия	Лист	Листов
							1
Руководитель	Клодт О.		22.01.2026				
ГАП	Юматов И.		22.01.2026	LYRA GRANDE консоль 805x546x400			
Вед. арх. ИИ	Клочихин И.		22.01.2026				
Архитектор			22.01.2026				